



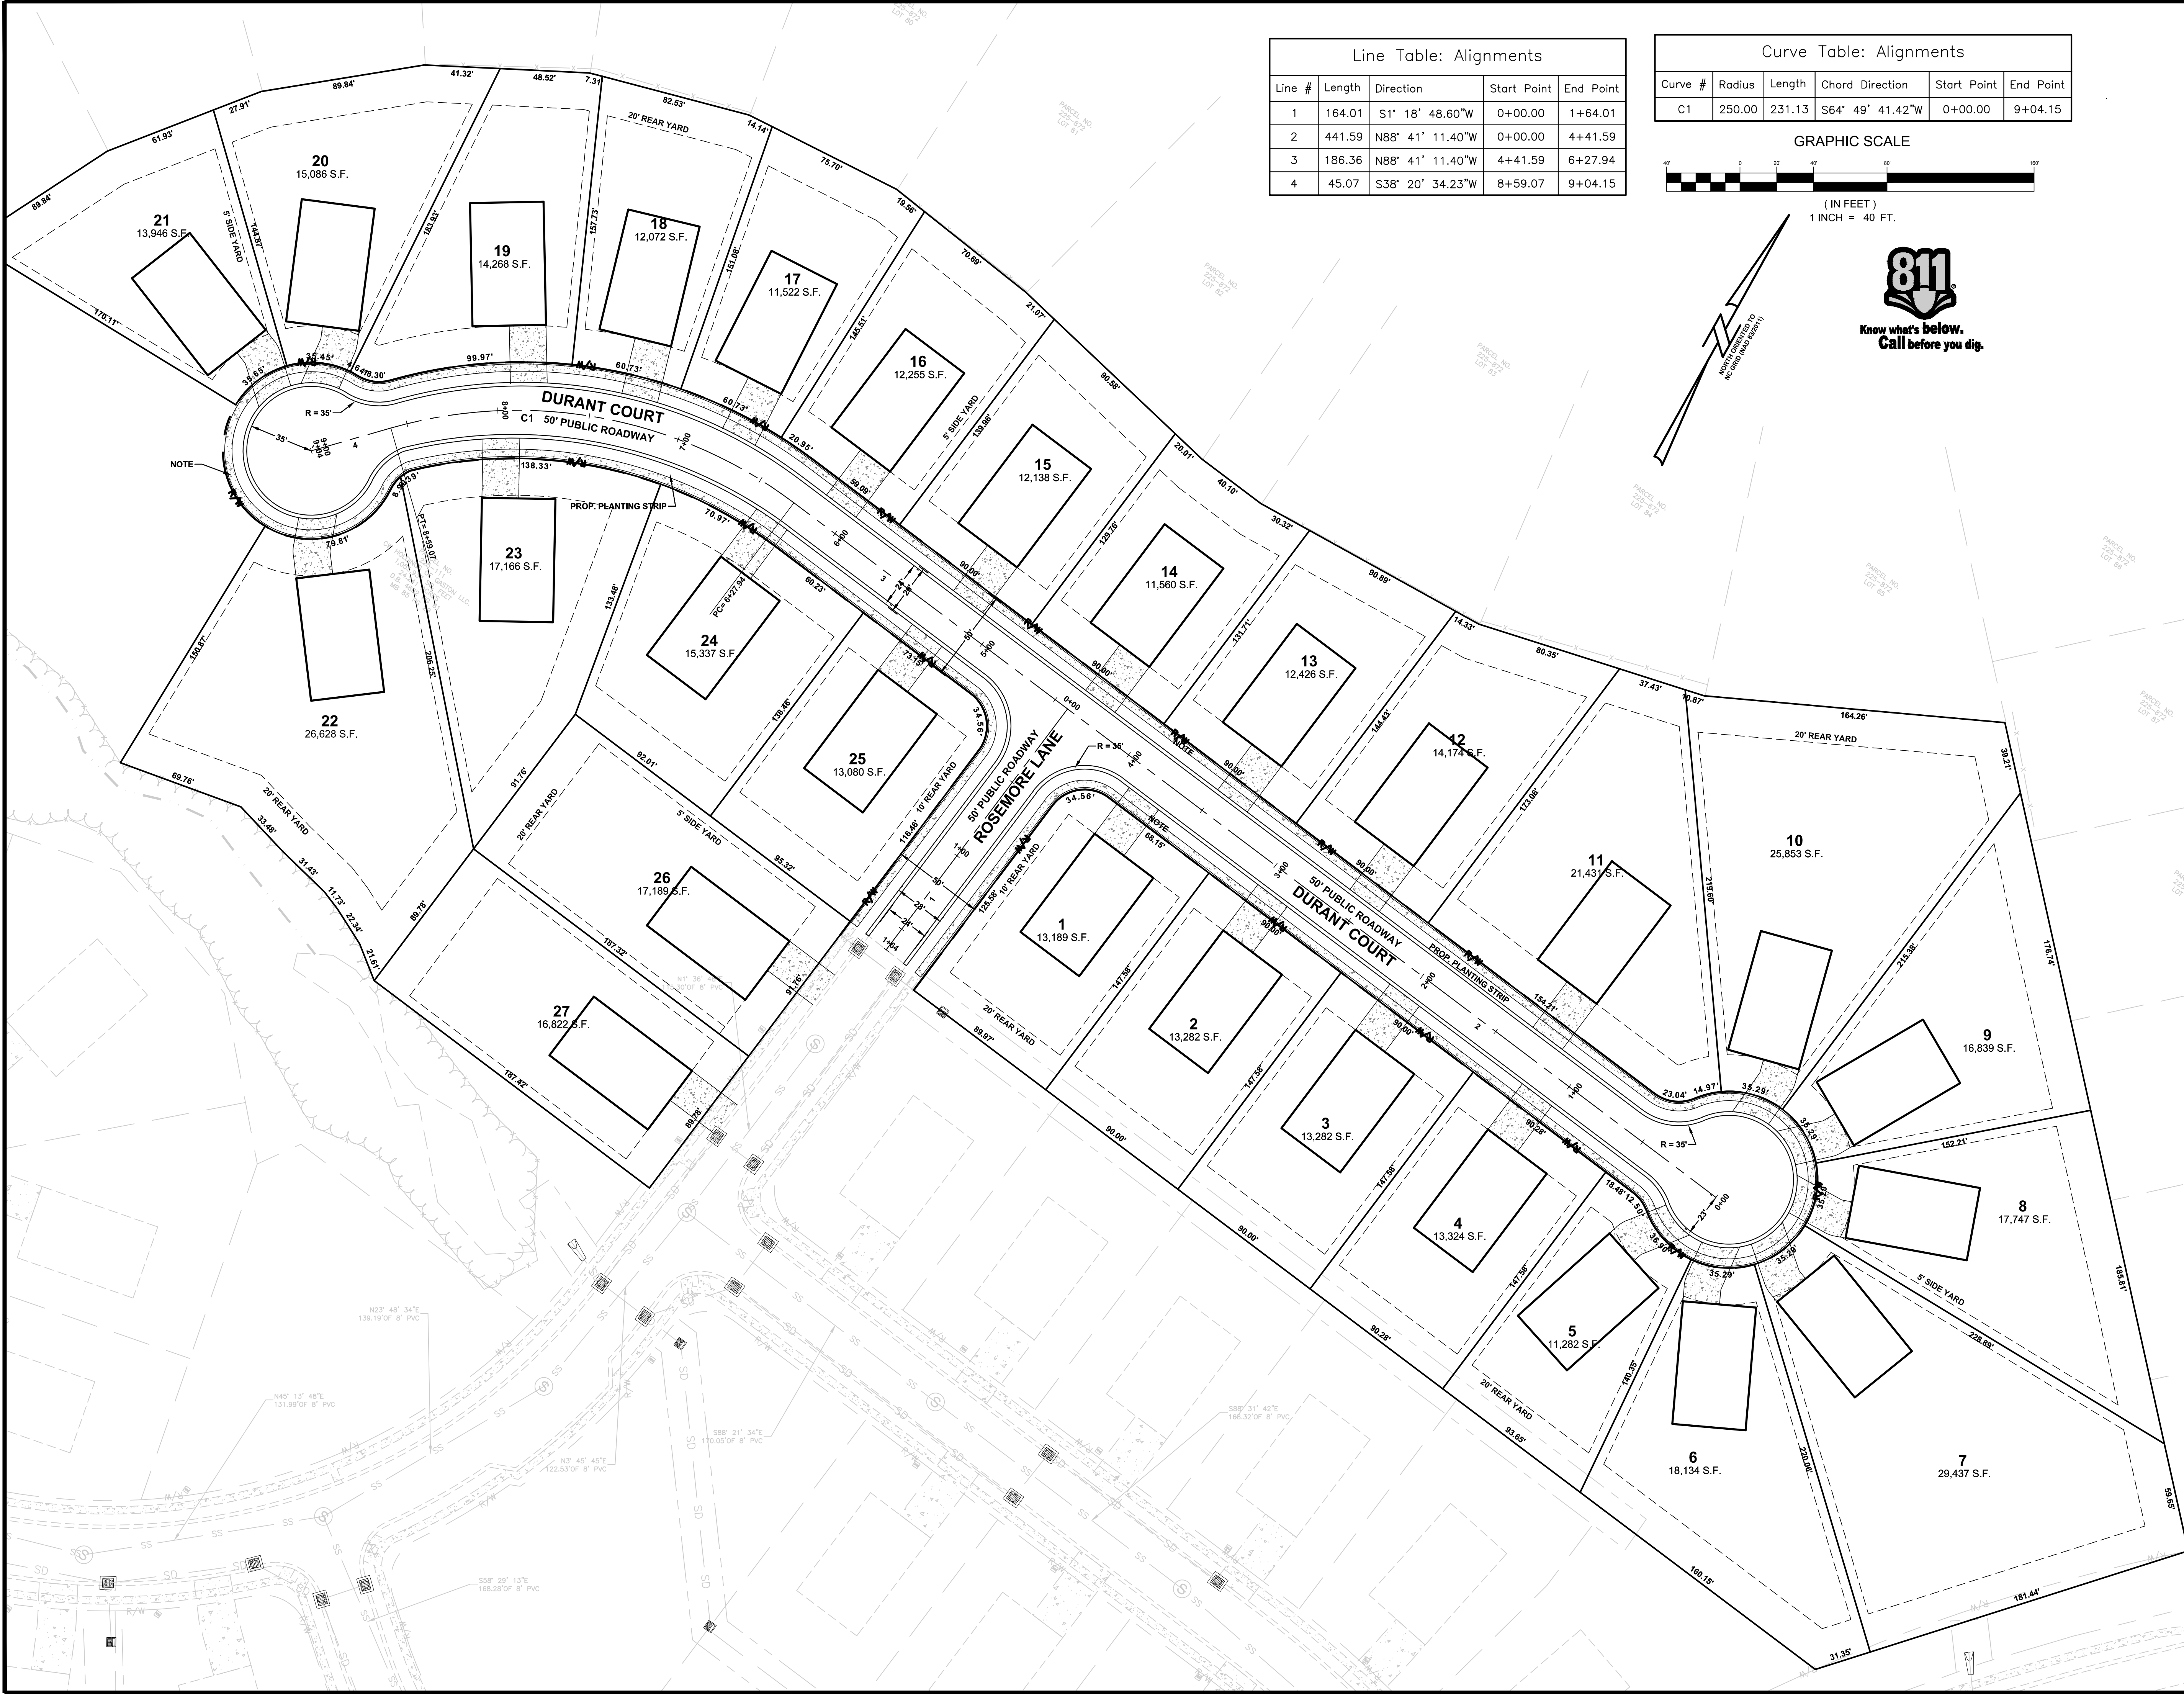

Line Table: Alignments					
Line #	Length	Direction	Start Point	End Point	
1	164.01	S1° 18' 48.60"W	0+00.00	1+64.01	
2	441.59	N88° 41' 11.40"W	0+00.00	4+41.59	
3	186.36	N88° 41' 11.40"W	4+41.59	6+27.94	
4	45.07	S38° 20' 34.23"W	8+59.07	9+04.15	

Curve Table: Alignments					
Curve #	Radius	Length	Chord Direction	Start Point	End Point
C1	250.00	231.13	S64° 49' 41.42"W	0+00.00	9+04.15

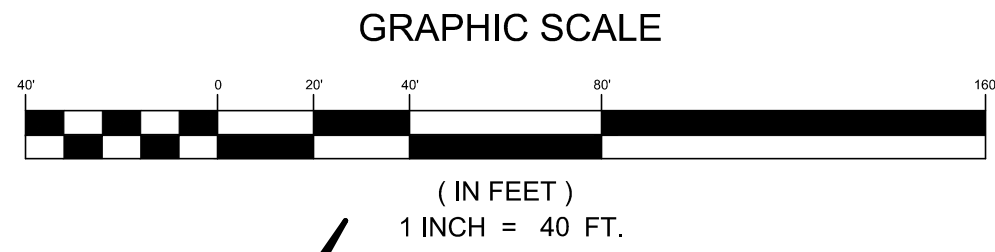

CENTRAL PIEDMONT
COMMUNITY COLLEGE

**PRELIMINARY
NOT FOR
CONSTRUCTION**

NO.	DATE	REVISION	BY

SHEET NAME
HOMEWORK 4

CLIENT: CPCC
GASTONIA, NORTH CAROLINA

PROJECT INFORMATION	
PROJECT MANAGER:	NSK
DESIGNED BY:	CMT
DRAWN BY:	CMT
PROJECT NUMBER:	XXXX
ORIGINAL DATE:	10/27/2025